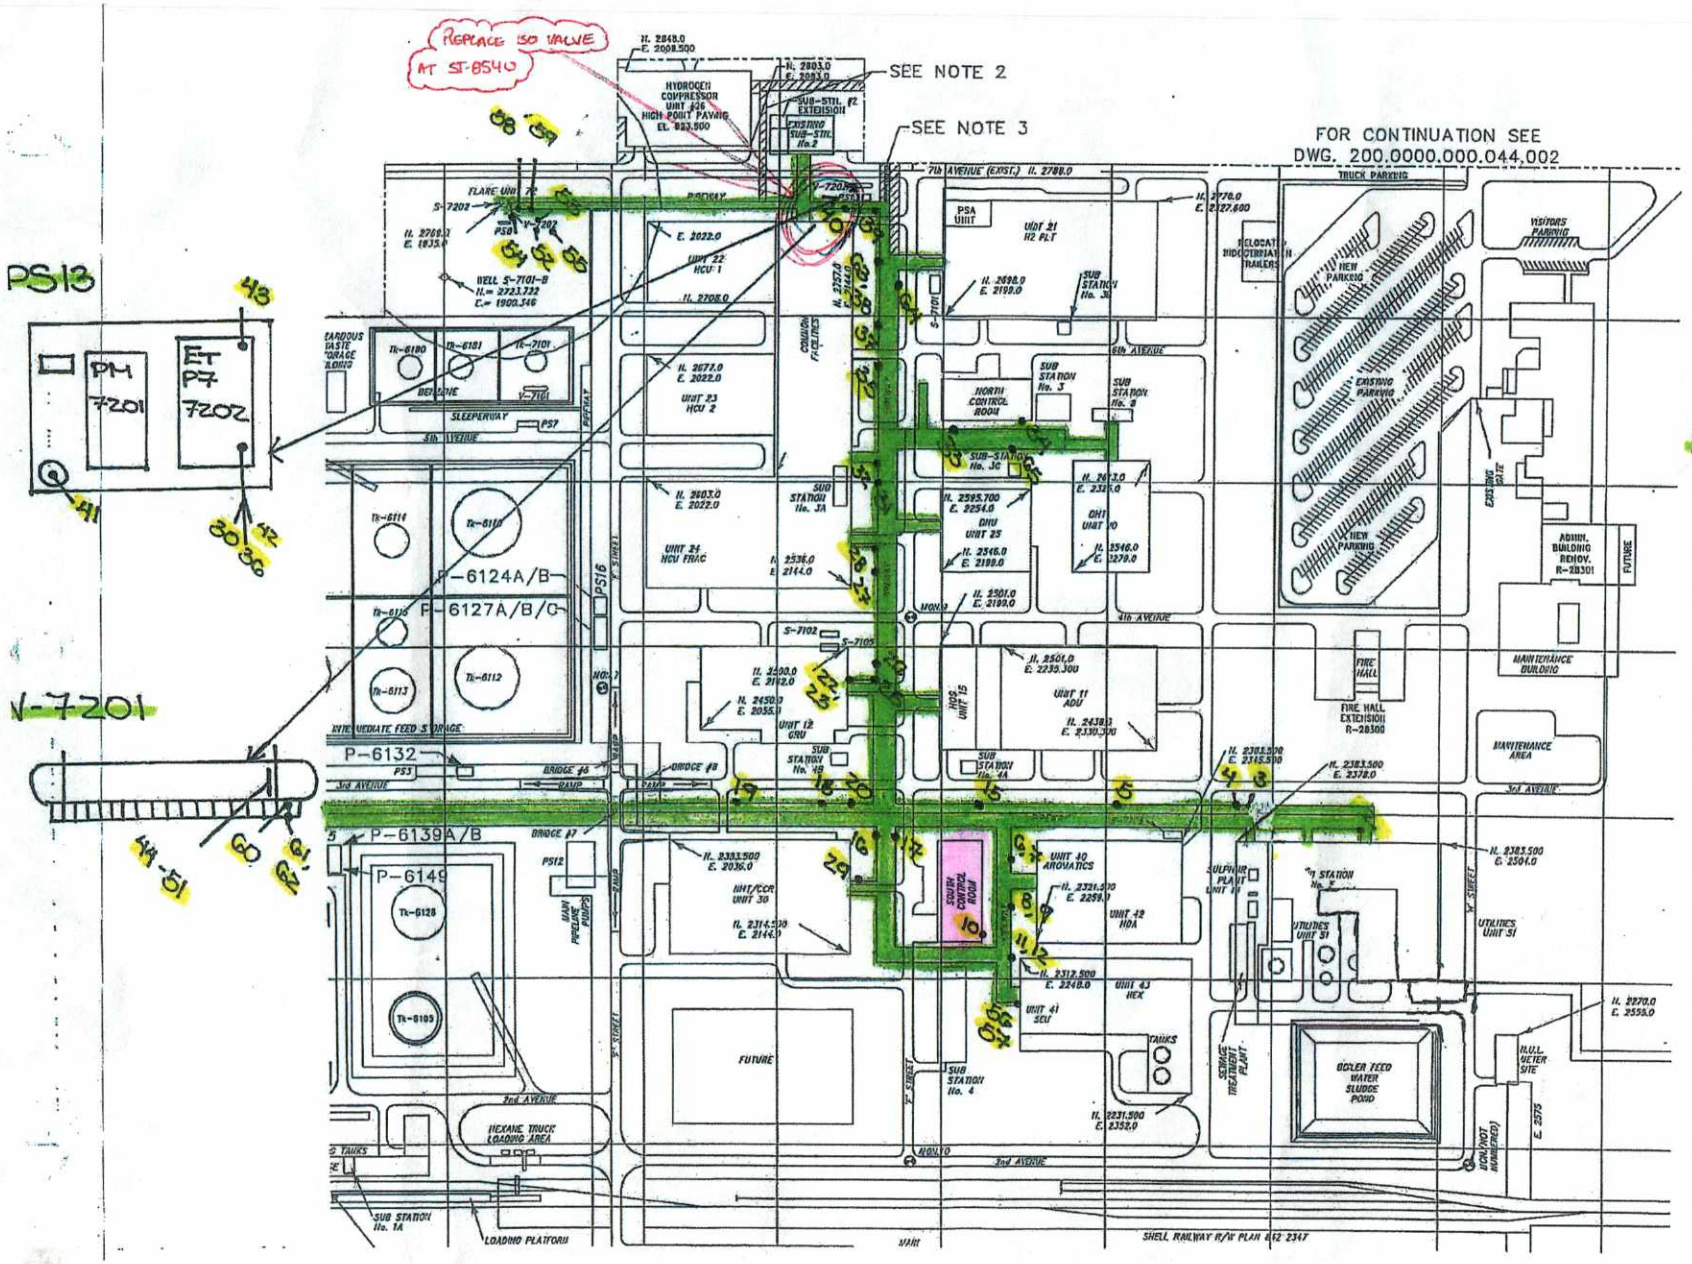
REPLACE ISO VALVE AT ST-8540
SEE NOTE 2
SEE NOTE 3
FOR CONTINUATION SEE DWG. 200.0000.000.044.002
PS13
PM 7201
ET P7 7202
V-7201
P-6124A/B
P-6127A/B/C
P-6132
P-6139A/B
P-6149
Tk-6114
Tk-6116
Tk-6113
Tk-6112
Tk-6128
Tk-6103
Tk-6190
Tk-6181
Tk-7101
HYDROGEN COMPRESSOR UNIT #36 HIGH POINT PAVING EL. 833.500
EXISTING SUB-STN. No. 2
SUB-STN. #2 EXTENSION
FLARE UNIT 72
WELL S-7101-B
UNIT 22 HCU 1
UNIT 23 HCU 2
UNIT 24 HCU FRAC
UNIT 21 H2 PLT
PSA UNIT
RELOCATABLE HIDROTRIATIN TRAILERS
SUB STATION No. 3
SUB STATION No. 3A
SUB STATION No. 3B
SUB STATION No. 3C
NORTH CONTROL ROOM
UNIT 25 DHU
UNIT 10 DHU
UNIT 11 ADU
UNIT 12 GHU
UNIT 15 HDS
SUB STATION No. 4A
SUB STATION No. 4B
SUB STATION No. 4
UNIT 40 AROMATICS
UNIT 42 HDA
UNIT 43 HEX
UNIT 41 SCU
UNIT 30 HHT/CCR
SOUTH CONTROL ROOM
SULPHUR PLANT UNIT 44
UTILITIES UNIT 51
TANKS
SEWAGE TREATMENT PLANT
BOILER FEED WATER SLUDGE POND
FUTURE
HEXANE TRUCK LOADING AREA
LOADING PLATFORM
SUB STATION No. 1A
TRUCK PARKING
VISITORS PARKING
NEW PARKING
EXISTING PARKING
ADMIN. BUILDING RENOV. R-28301
MAINTENANCE BUILDING
MAINTENANCE AREA
FIRE HALL
FIRE HALL EXTENSION R-28300
EXISTING GATE
N.U.L. METER SITE
7th AVENUE (EXIST.)
6th AVENUE
5th AVENUE
4th AVENUE
3rd AVENUE
2nd AVENUE
SLEEPERWAY
BRIDGE #5
BRIDGE #6
BRIDGE #7
BRIDGE #8
RAMP
MAIN PIPELINE CORRIDOR
SHELL RAILWAY R/W PLAN 412 2347
Back 85
Steam Trap Locations

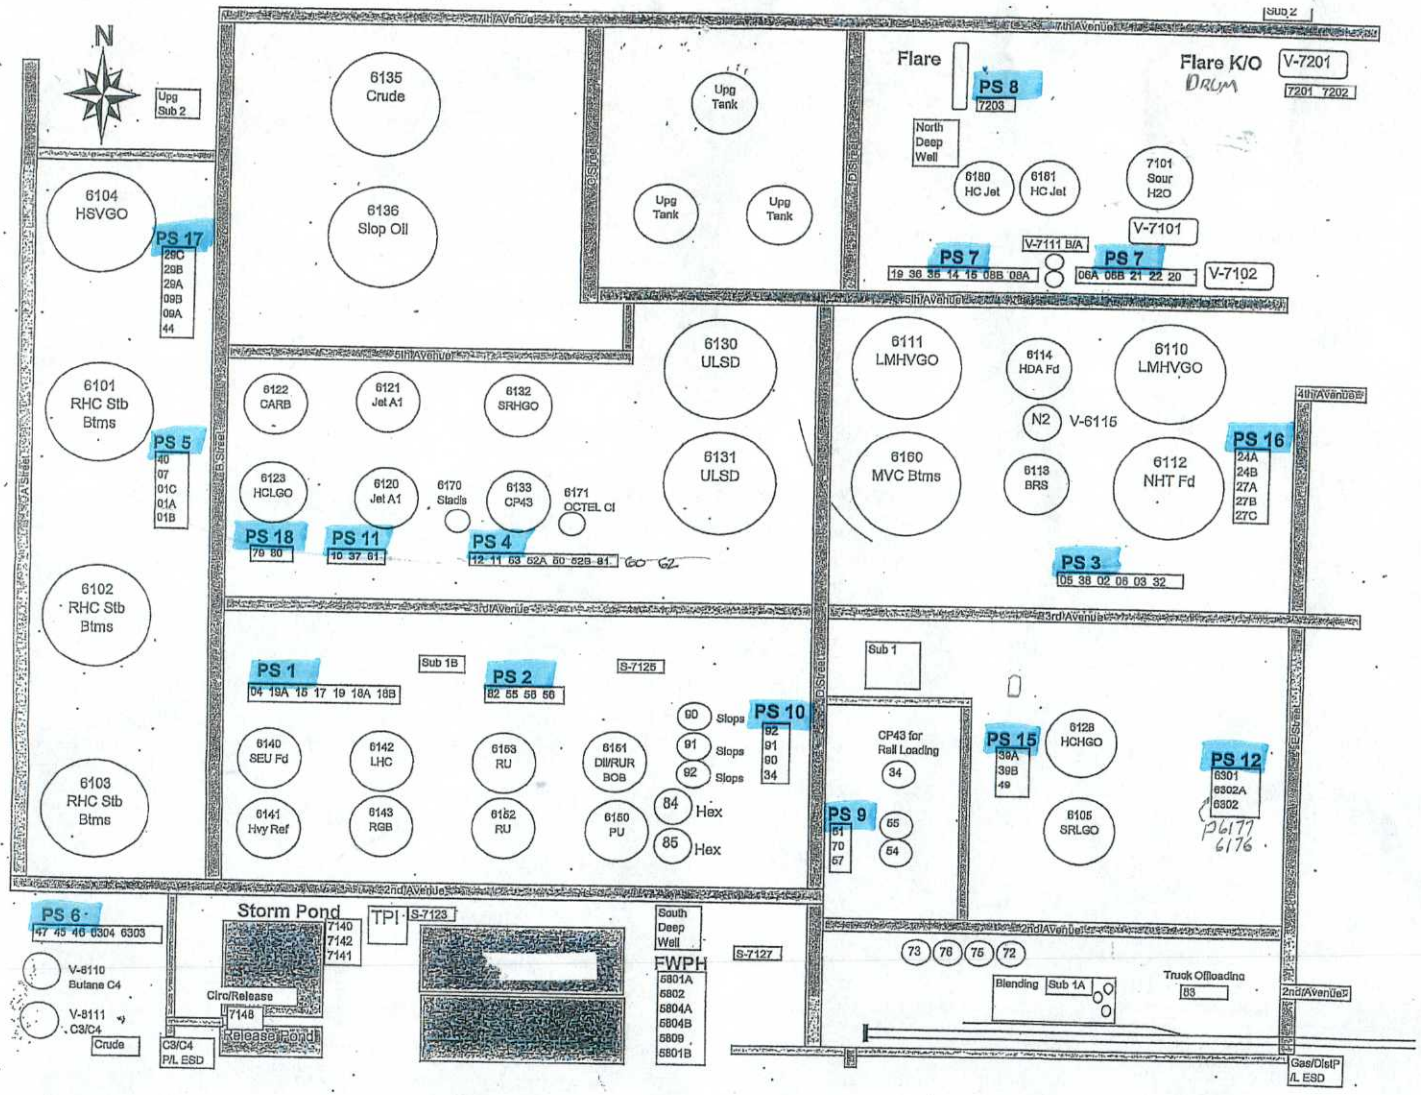
N
Upg Sub 2
6135 Crude
6136 Slop Oil
Upg Tank
Upg Tank
Upg Tank
Flare
PS 8
7203
Flare K/O
DRUM
V-7201
7201 7202
North Deep Well
6180 HC Jet
6181 HC Jet
7101 Sour H2O
V-7101
V-7111 B/A
PS 7
19 36 35 14 15 08B 08A
PS 7
06A 06B 21 22 20
V-7102
6104 HSVGO
PS 17
28C
29B
29A
09B
09A
44
6101 RHC Stb Btms
PS 5
30
07
01C
01A
01B
6102 RHC Stb Btms
6103 RHC Stb Btms
6122 CARB
6121 Jet A1
6132 SRHGO
6123 HCLGO
6120 Jet A1
6170 Stadis
6133 CP43
6171 OCTEL CI
PS 18
79 80
PS 11
10 37 61
PS 4
12 11 53 52A 50 52B 81
6130 ULSD
6131 ULSD
6111 LMHVGO
6114 HDA Fd
6110 LMHVGO
N2
V-6115
6160 MVC Btms
6113 BRS
6112 NHT Fd
PS 16
24A
24B
27A
27B
27C
PS 3
05 38 02 08 03 32
PS 1
04 19A 15 17 19 18A 18B
Sub 1B
PS 2
82 55 56 58
S-7125
90 Slops
91 Slops
92 Slops
PS 10
92
91
90
34
6140 SEU Fd
6142 LHC
6163 RU
6161 DII/RUR BOB
6141 Hvy Ref
6143 RGB
6162 RU
6160 PU
84 Hex
85 Hex
Sub 1
CP43 for Rail Loading
34
PS 9
61
70
57
55
54
PS 15
39A
39B
49
6128 HCHGO
6105 SRLGO
PS 12
6301
6302A
6302
P6177
6176
PS 6
47 45 46 6304 6303
V-8110 Butane C4
V-8111 C3/C4
Crude
Storm Pond
7140
7142
7141
TPI
S-7123
Circ/Release
7148
Release Pond
C3/C4 P/L ESD
South Deep Well
FWPH
5801A
5802
5804A
5804B
5809
5801B
S-7127
73 76 75 72
Blending
Sub 1A
Truck Offloading
83
Gas/Distp /L ESD
Sub 2
7th Avenue
6th Avenue
5th Avenue
4th Avenue
3rd Avenue
2nd Avenue
1st Avenue
B Street
D Street
E Street